


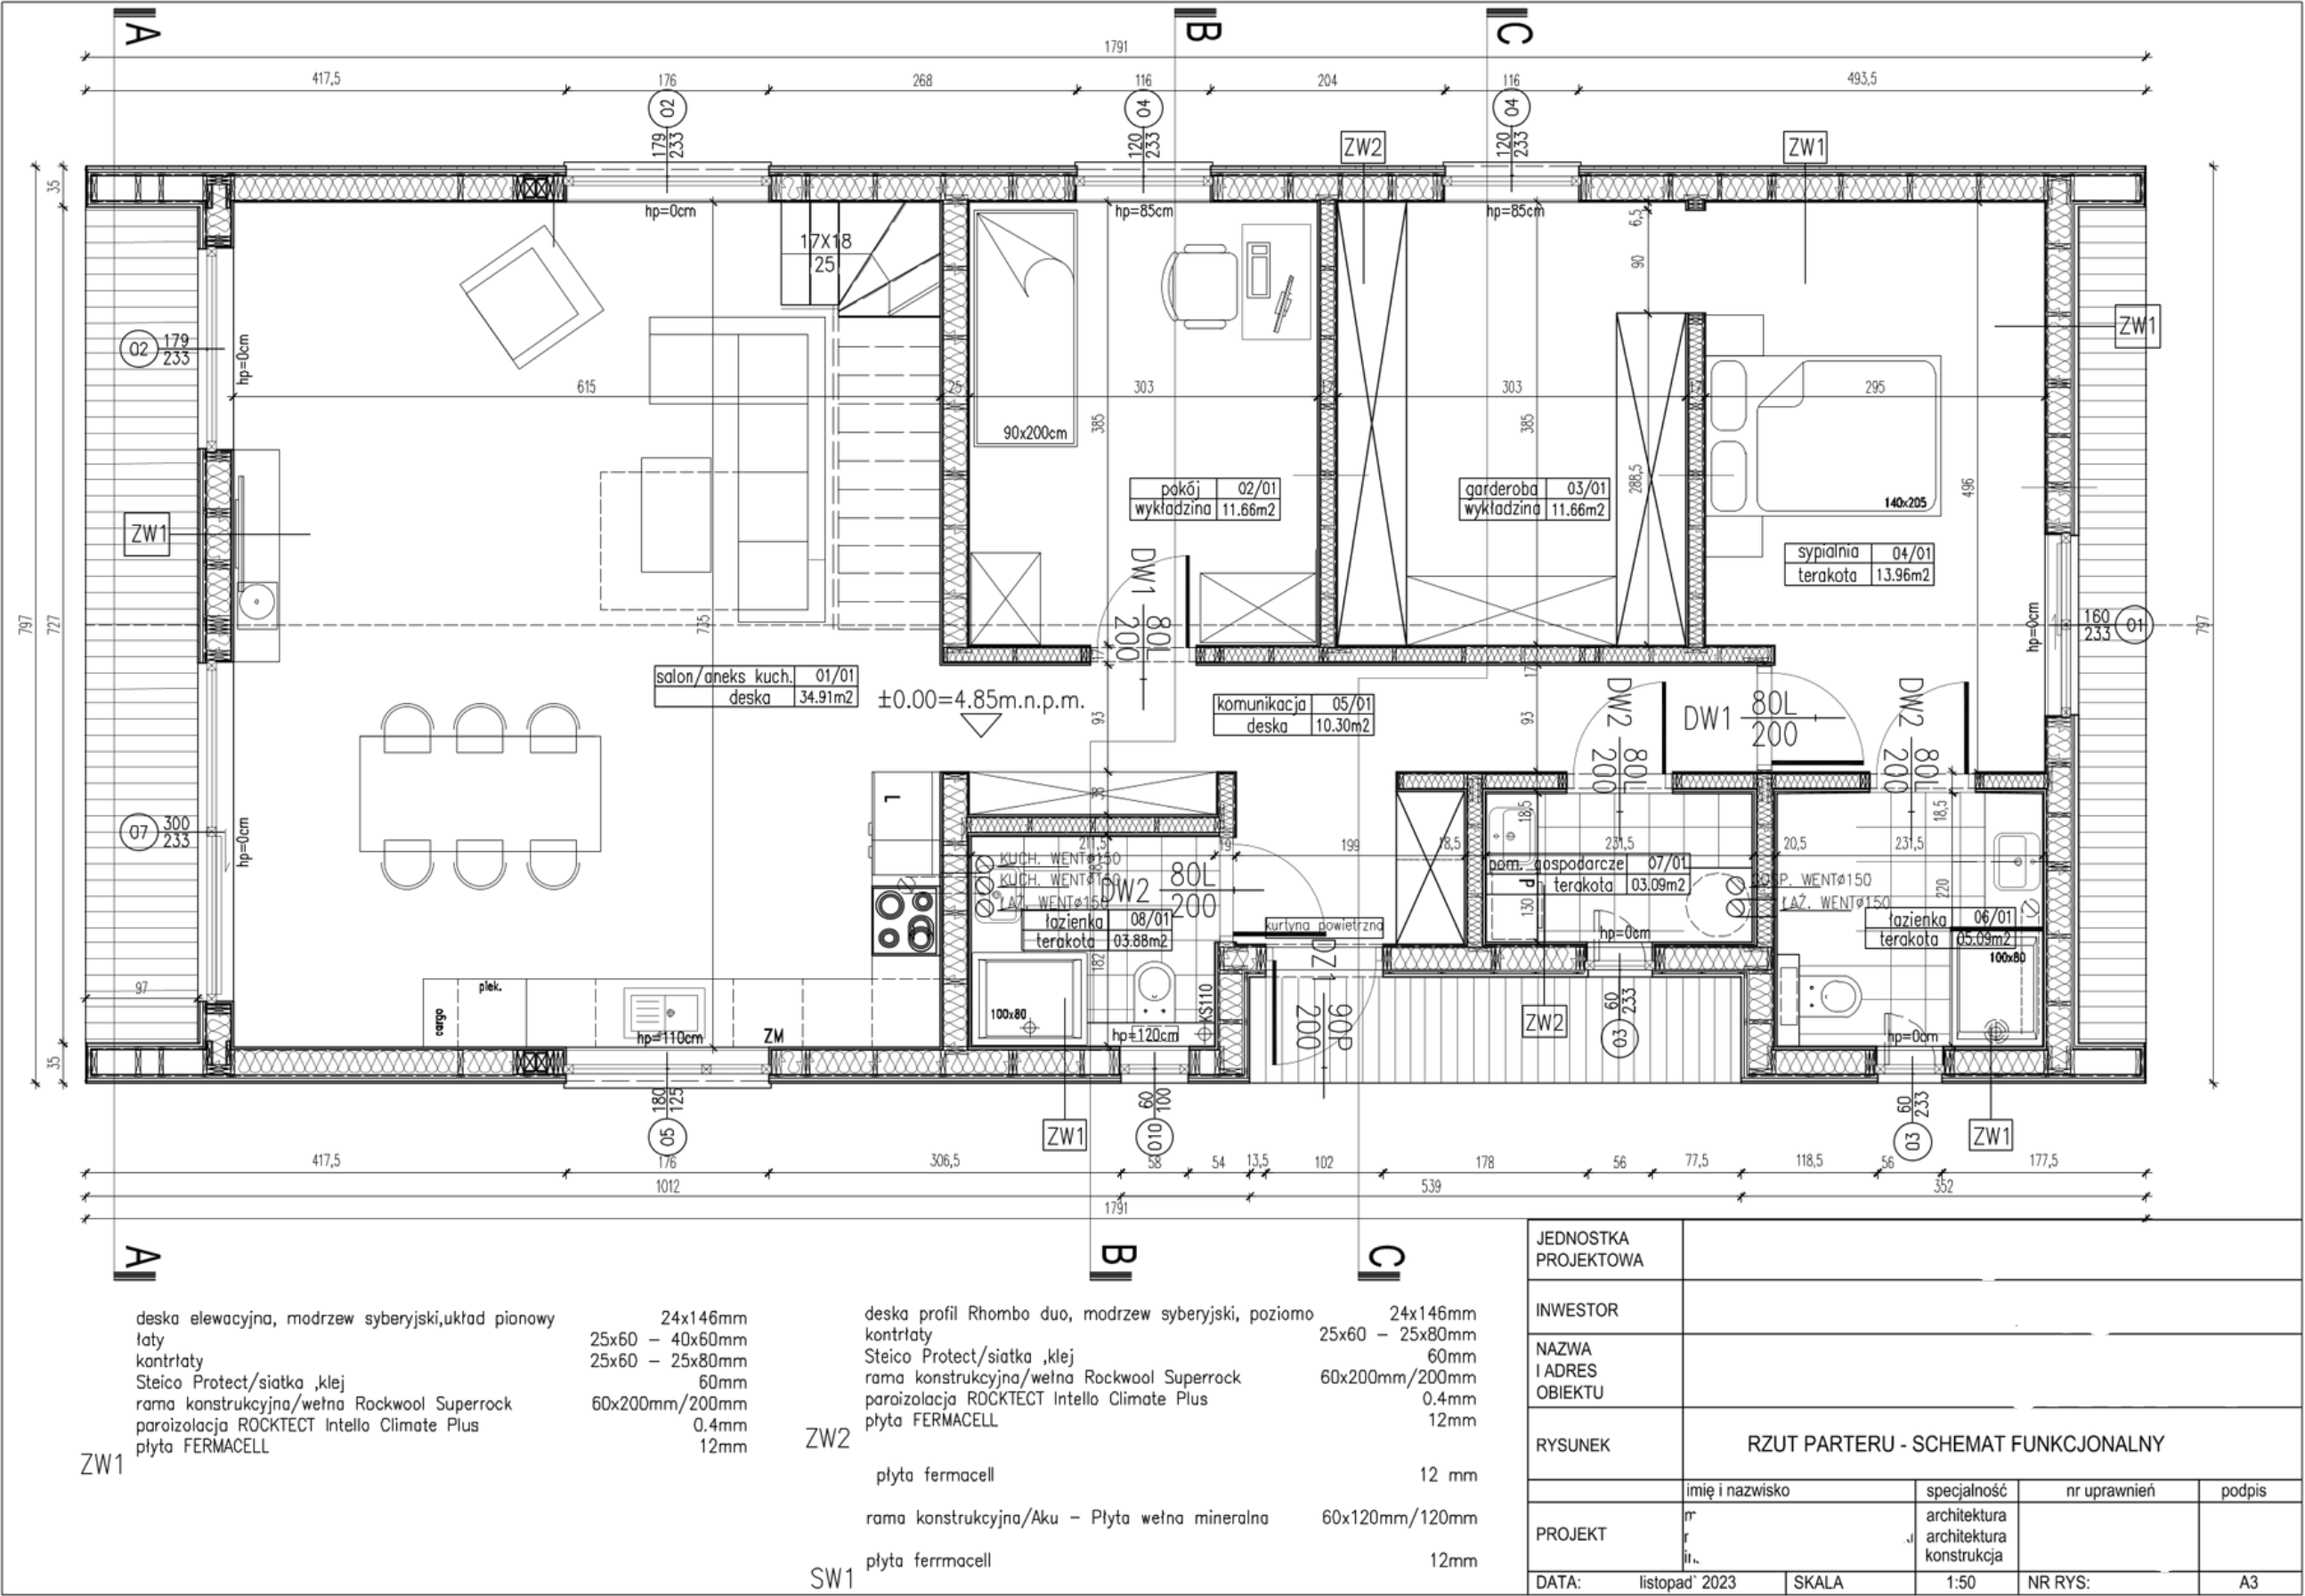

deska elewacyjna, modrzew syberyjski,układ pionowy
laty
kontrłaty
Steico Protect/siatka ,klej
rama konstrukcyjna/wełna Rockwool Superrock
paraizolacja ROCKTECT Intello Climate Plus
plyta FERMACELL

24x146mm
25x60 – 40x60mm
25x60 – 25x80mm
60mm
60x200mm/200mm
0.4mm
12mm

deska profil Rhombo duo, modrzew syberyjski, poziomo
kontrłaty
Steico Protect/siatka ,klej
rama konstrukcyjna/wełna Rockwool Superrock
paraizolacja ROCKTECT Intello Climate Plus
plyta FERMACELL

24x146mm
25x60 – 25x80mm
60mm
60x200mm/200mm
0.4mm
12mm

plyta fermacell 12 mm
rama konstrukcyjna/Aku – Plyta wełna mineralna 60x120mm/120mm
plyta fermacell 12mm

JEDNOSTKA PROJEKTOWA				
INWESTOR				
NAZWA I ADRES OBIEKTU				
RYSunek	RZUT PARTERU - SCHEMAT FUNKCJONALNY			
PROJEKT	imię i nazwisko	specjalność	nr uprawnień	podpis
	nr	architektura		
	li.	architektura		
		konstrukcja		
DATA:	listopad' 2023	SKALA	1:50	NR RYS:
				A3